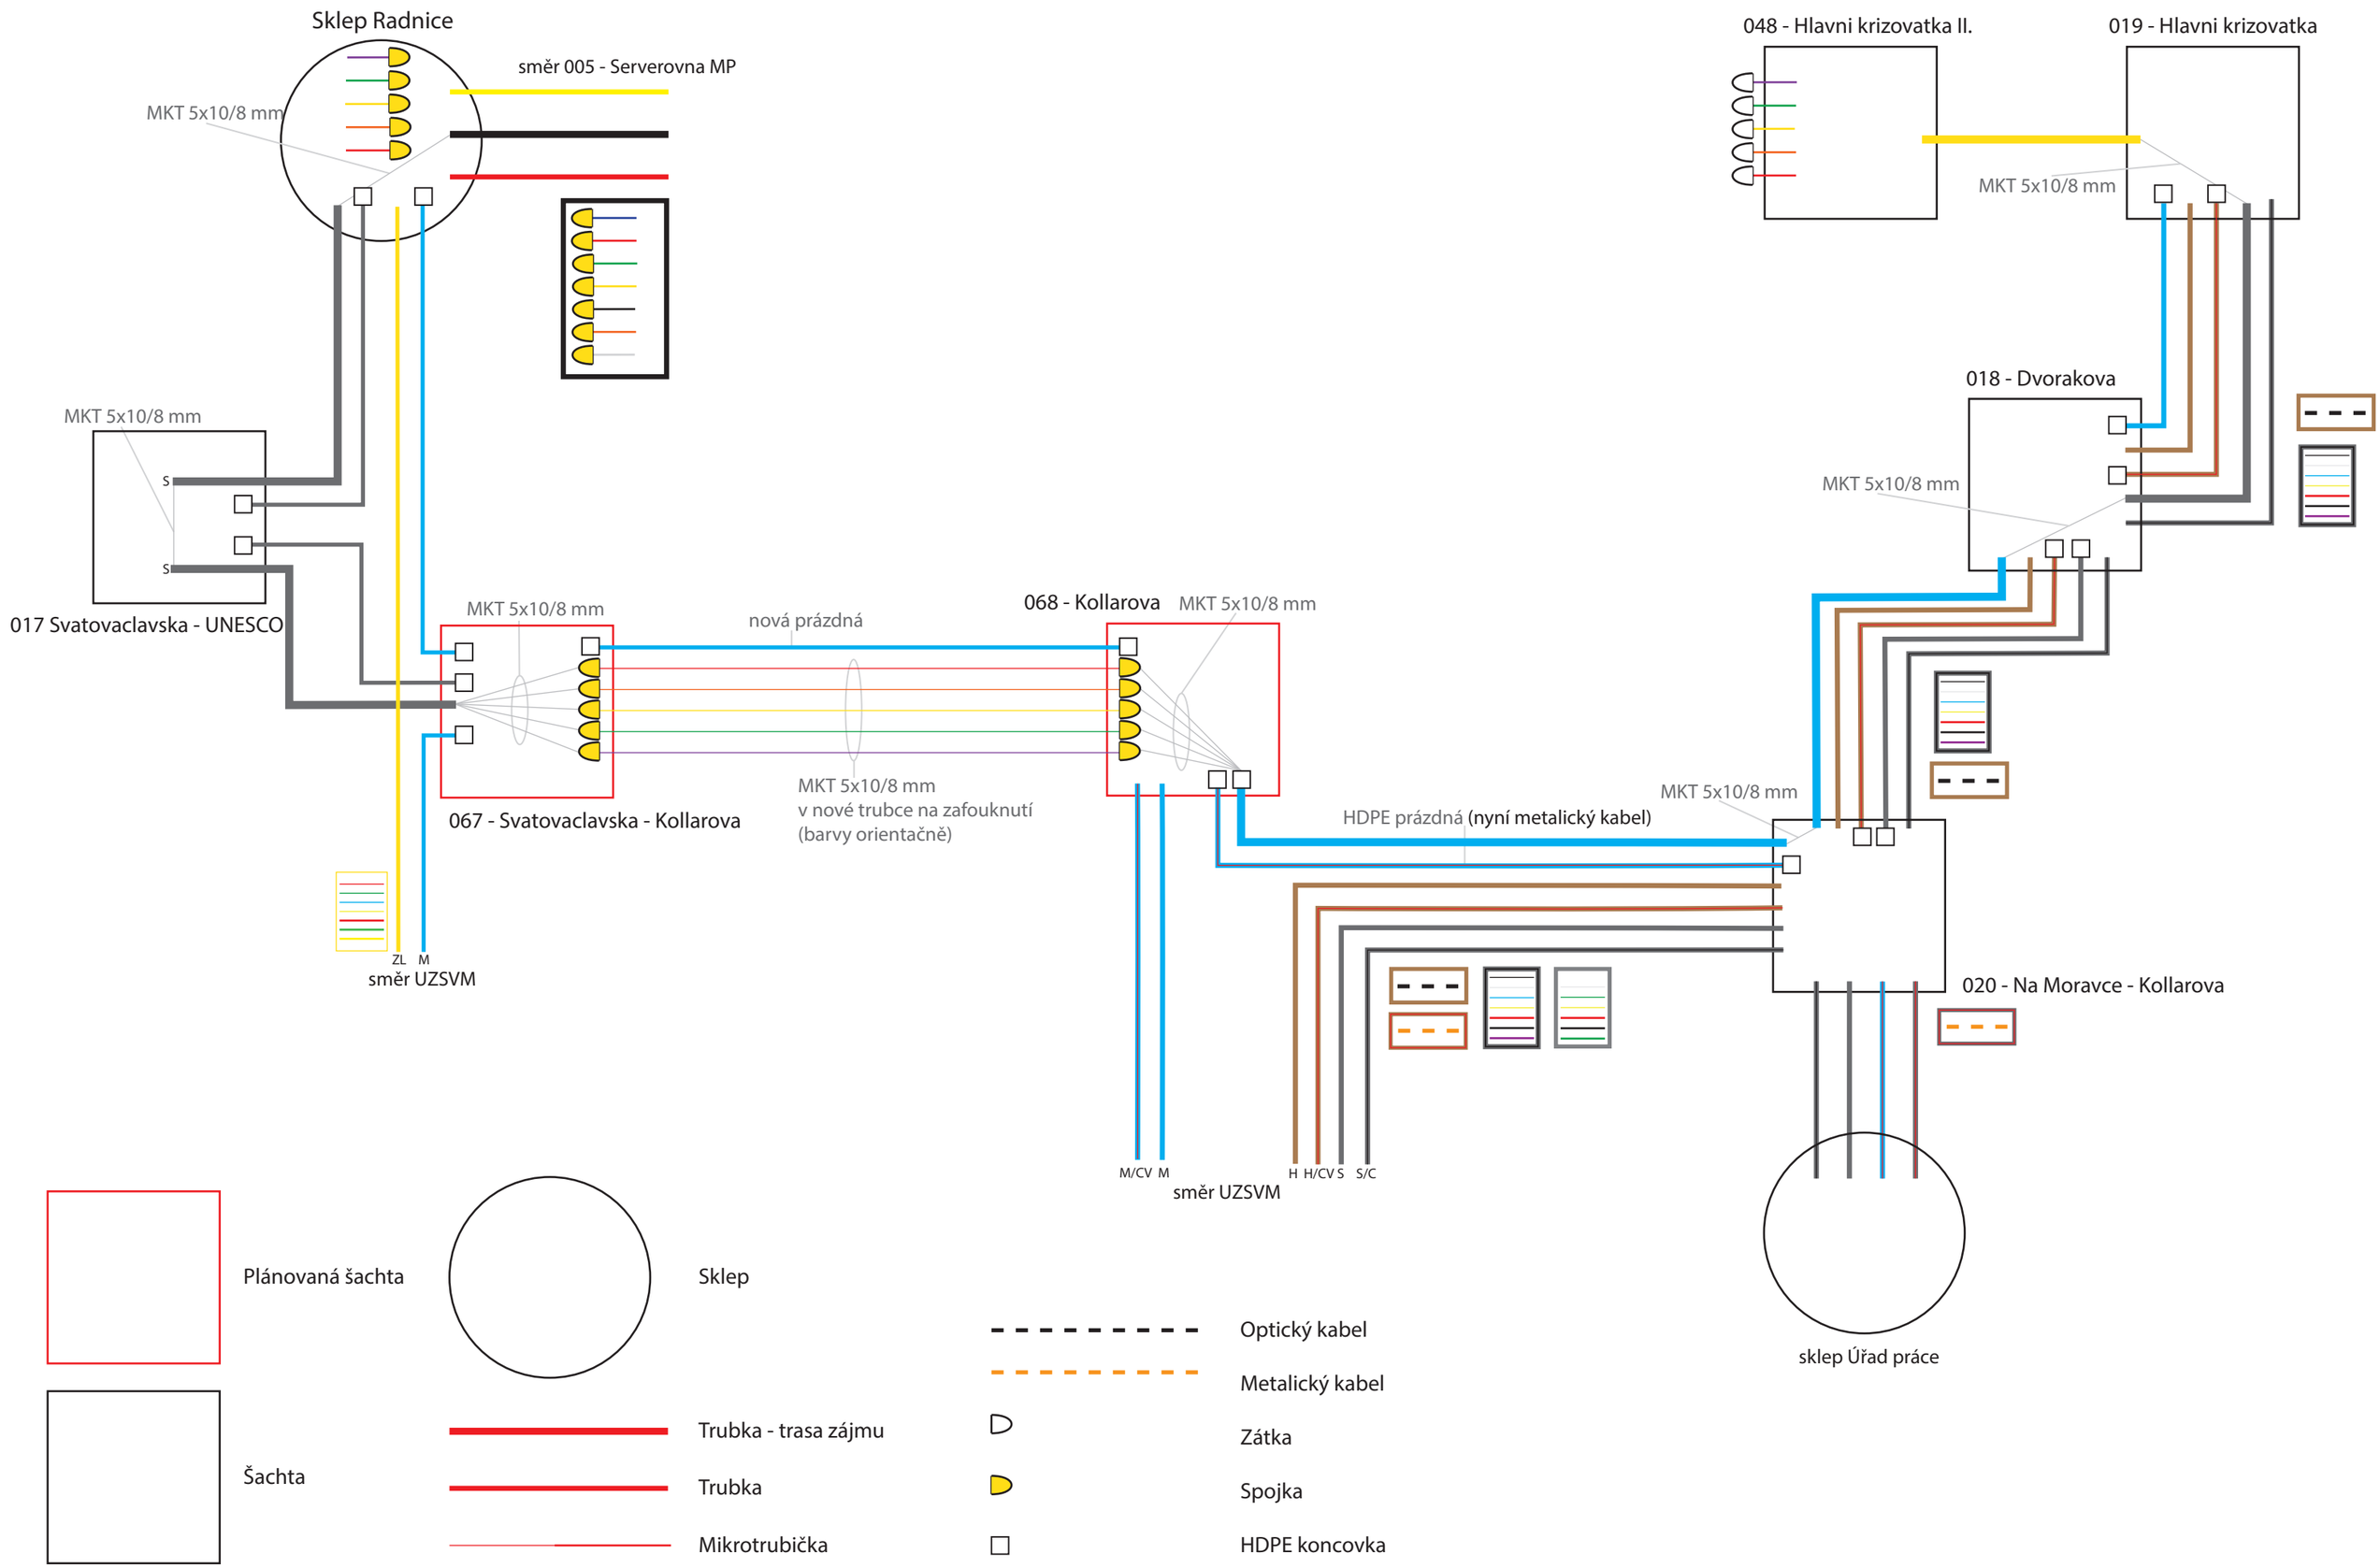
Sklep Radnice
směr 005 - Serverovna MP
MKT 5x10/8 mm
MKT 5x10/8 mm
S
S
017 Svatovaclavska - UNESCO
MKT 5x10/8 mm
067 - Svatovaclavska - Kollarova
nová prázdná
MKT 5x10/8 mm
v nové trubce na zafouknutí
(barvy orientačně)
068 - Kollarova
MKT 5x10/8 mm
ZL M
směr UZSVM
M/CV M
směr UZSVM
048 - Hlavni krizovatka II.
019 - Hlavni krizovatka
MKT 5x10/8 mm
018 - Dvorakova
MKT 5x10/8 mm
MKT 5x10/8 mm
HDPE prázdná (nyní metalický kabel)
020 - Na Moravce - Kollarova
H H/CV S S/C
sklep Úřad práce
Plánovaná šachta
Sklep
Šachta
Trubka - trasa zájmu
Trubka
Mikrotrubička
Optický kabel
Metalický kabel
Zátka
Spojka
HDPE koncovka